


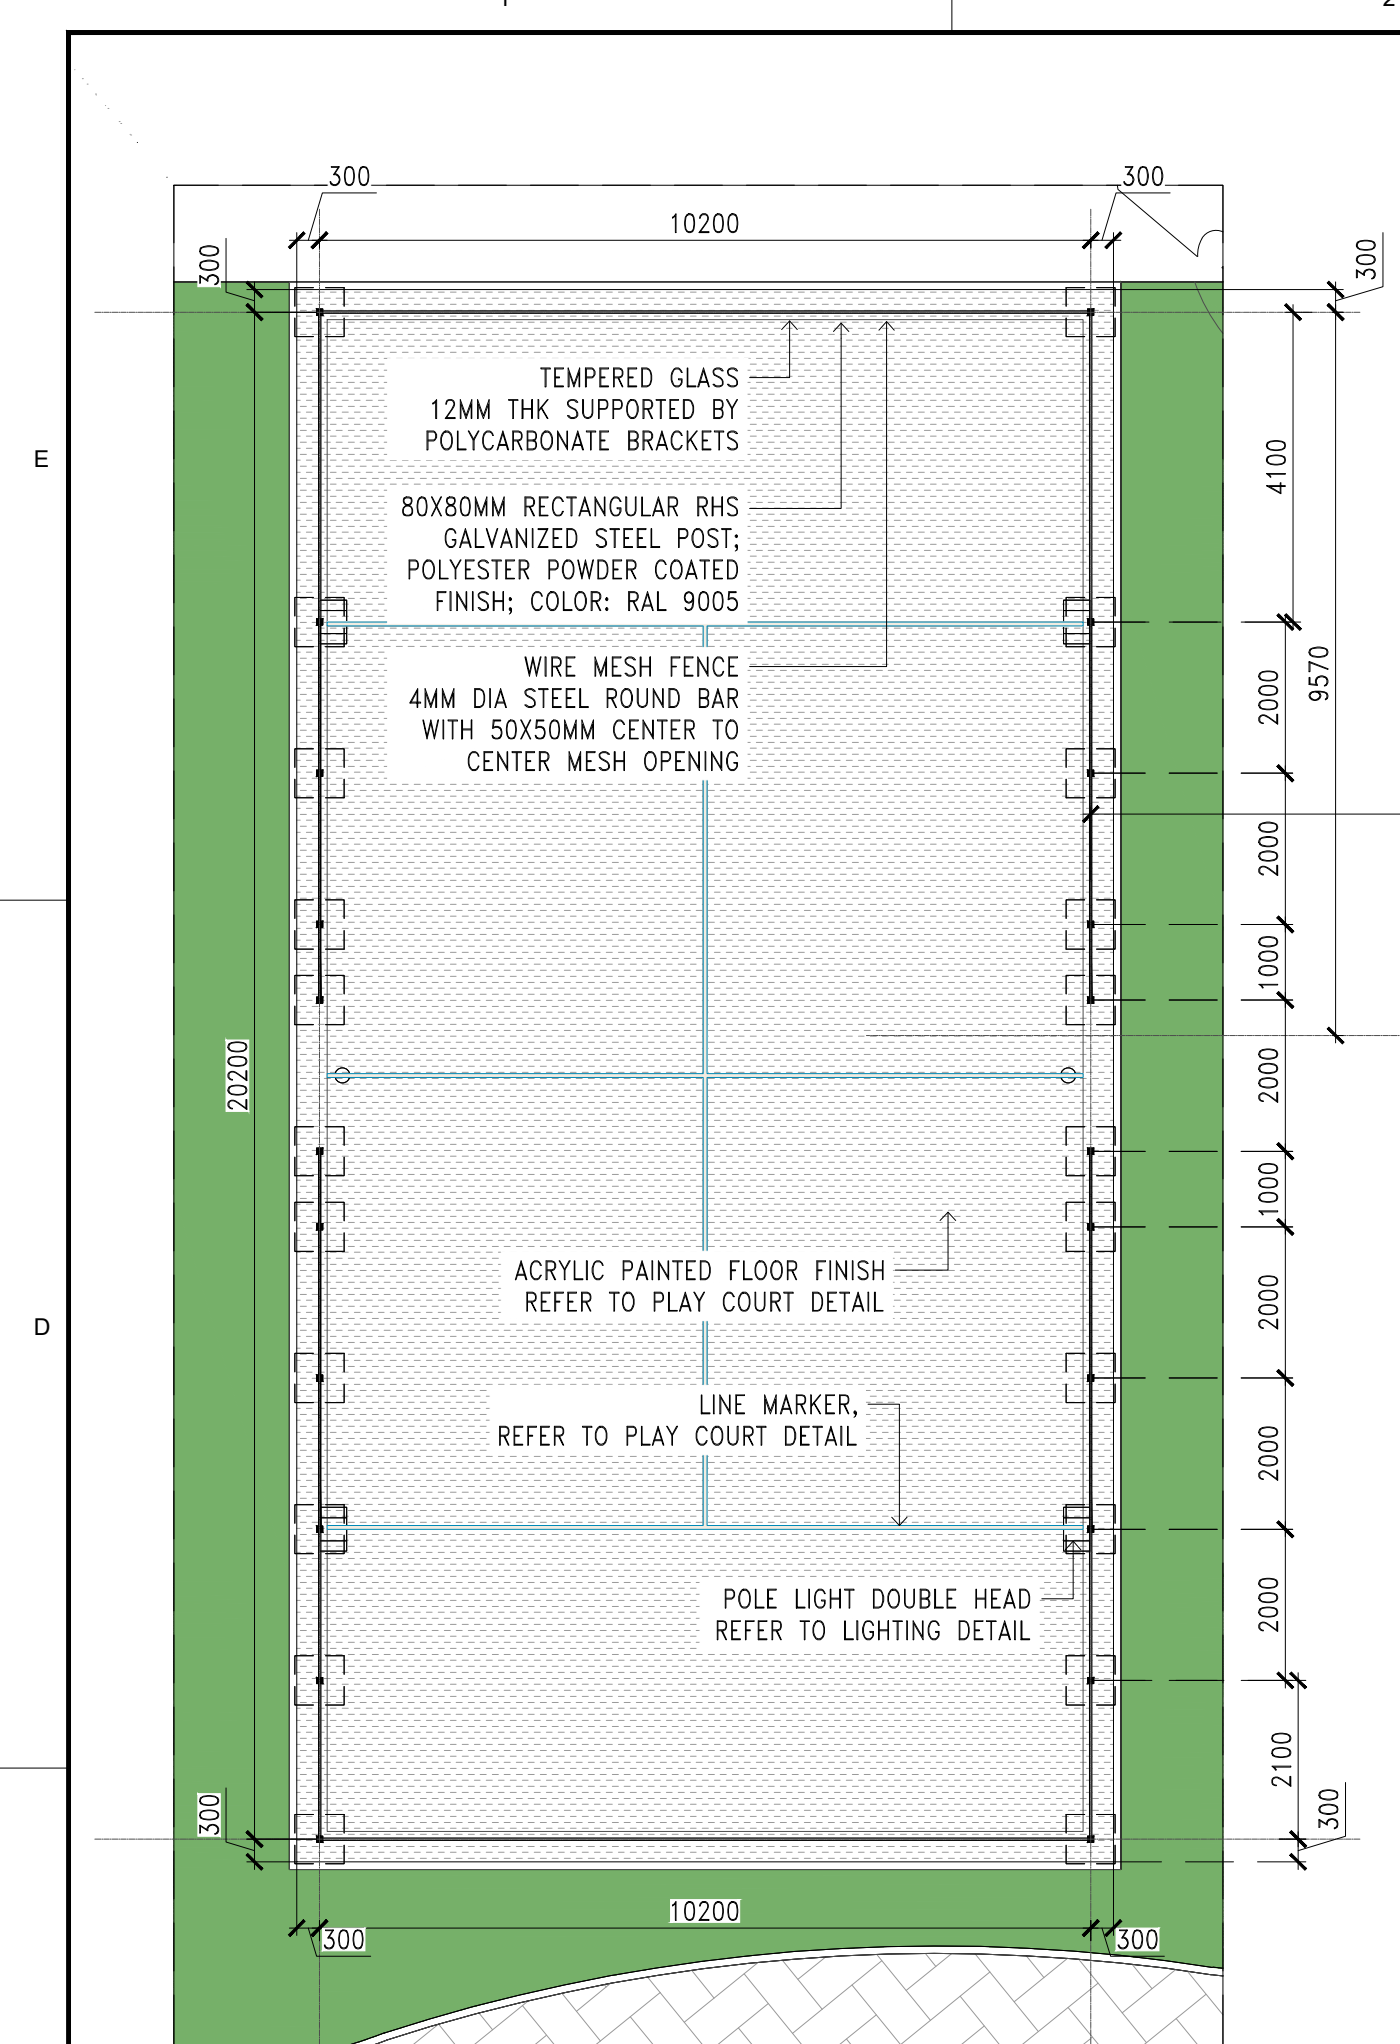


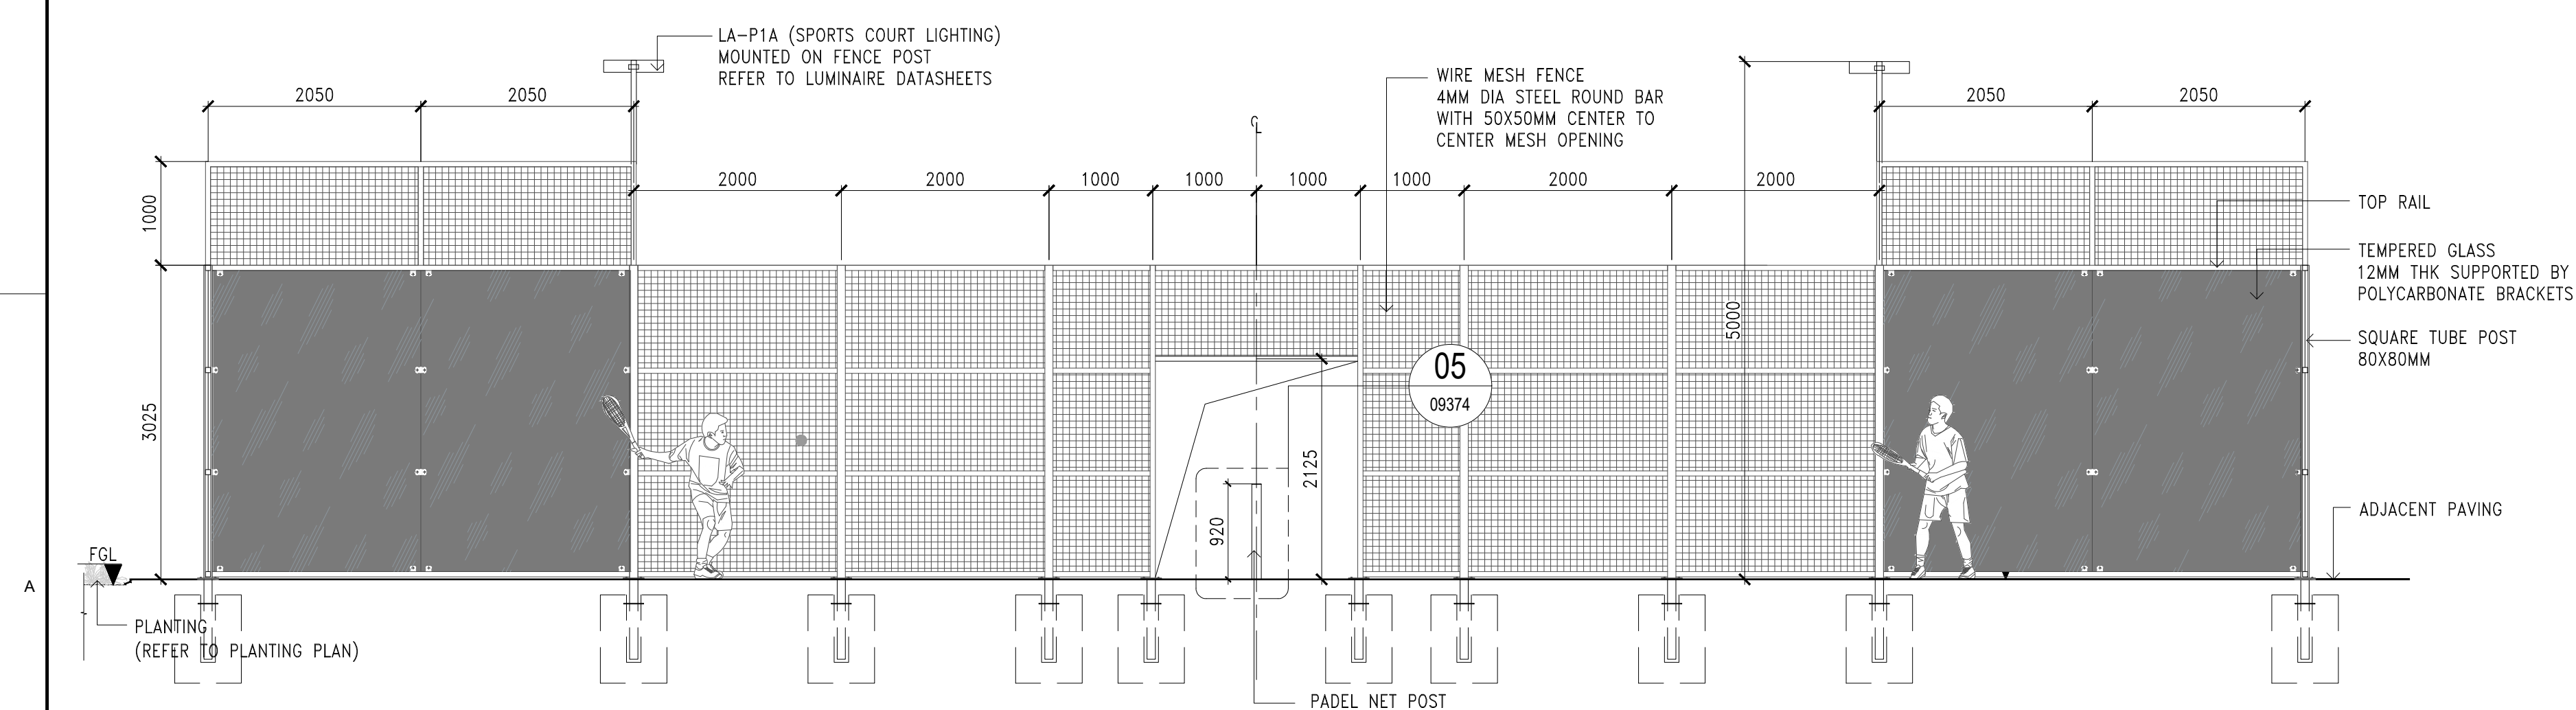


01 F07 - PADEL TENNIS FENCE DETAIL-PLAN
09374 SPORTS HUB
Scale 1:100

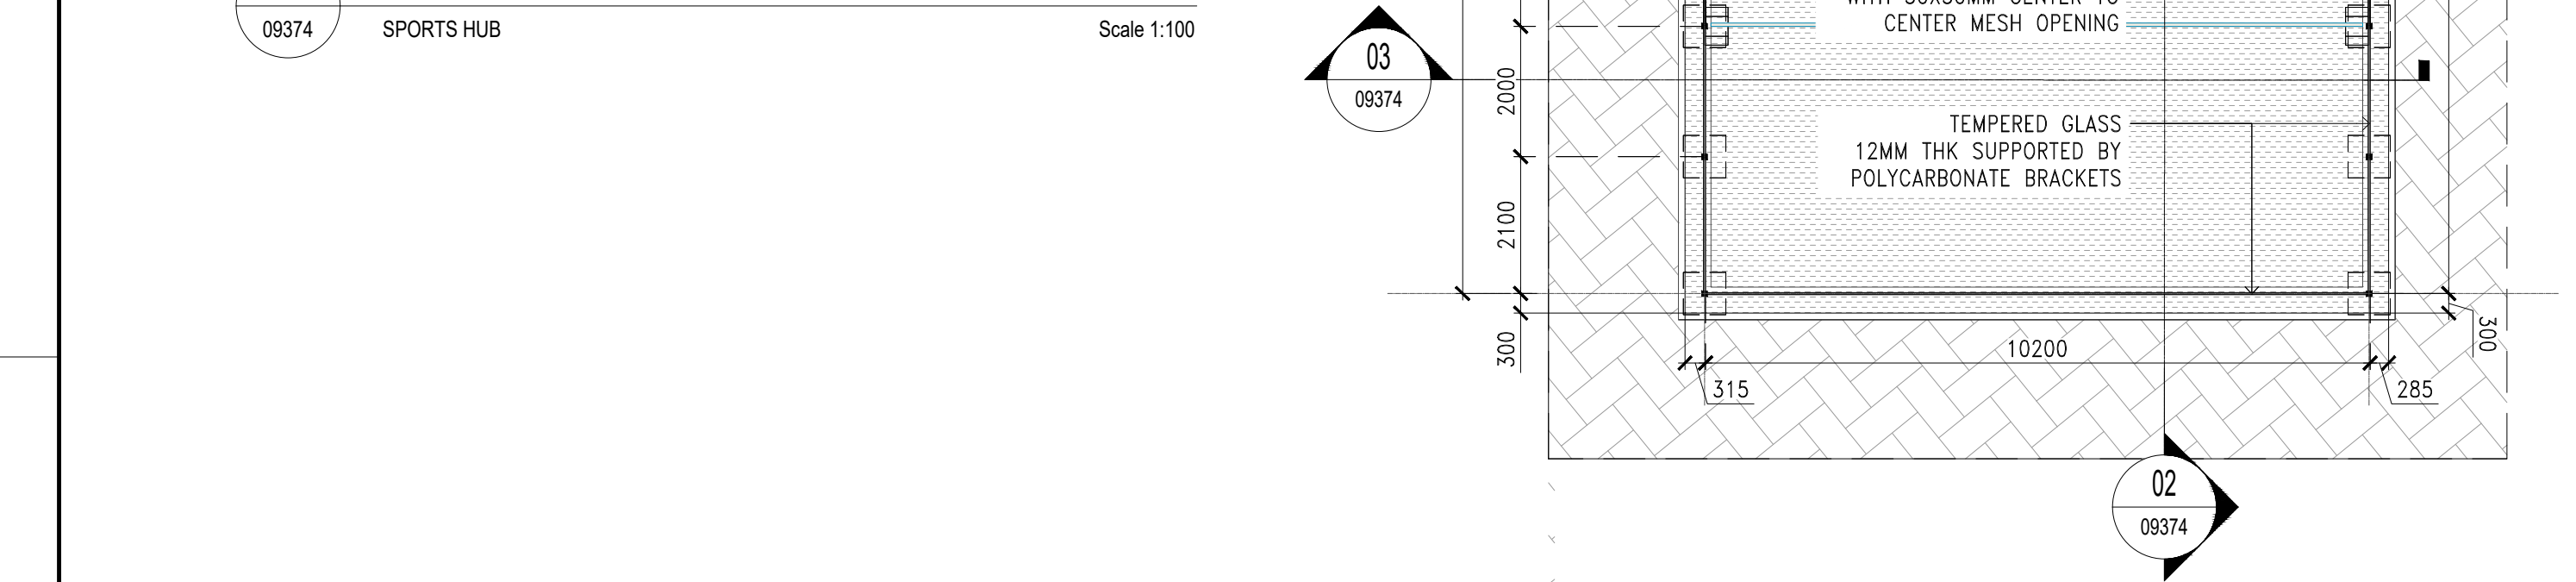


02 F07 - PADEL TENNIS FENCE DETAIL
09374 SPORTS HUB
Scale 1:50

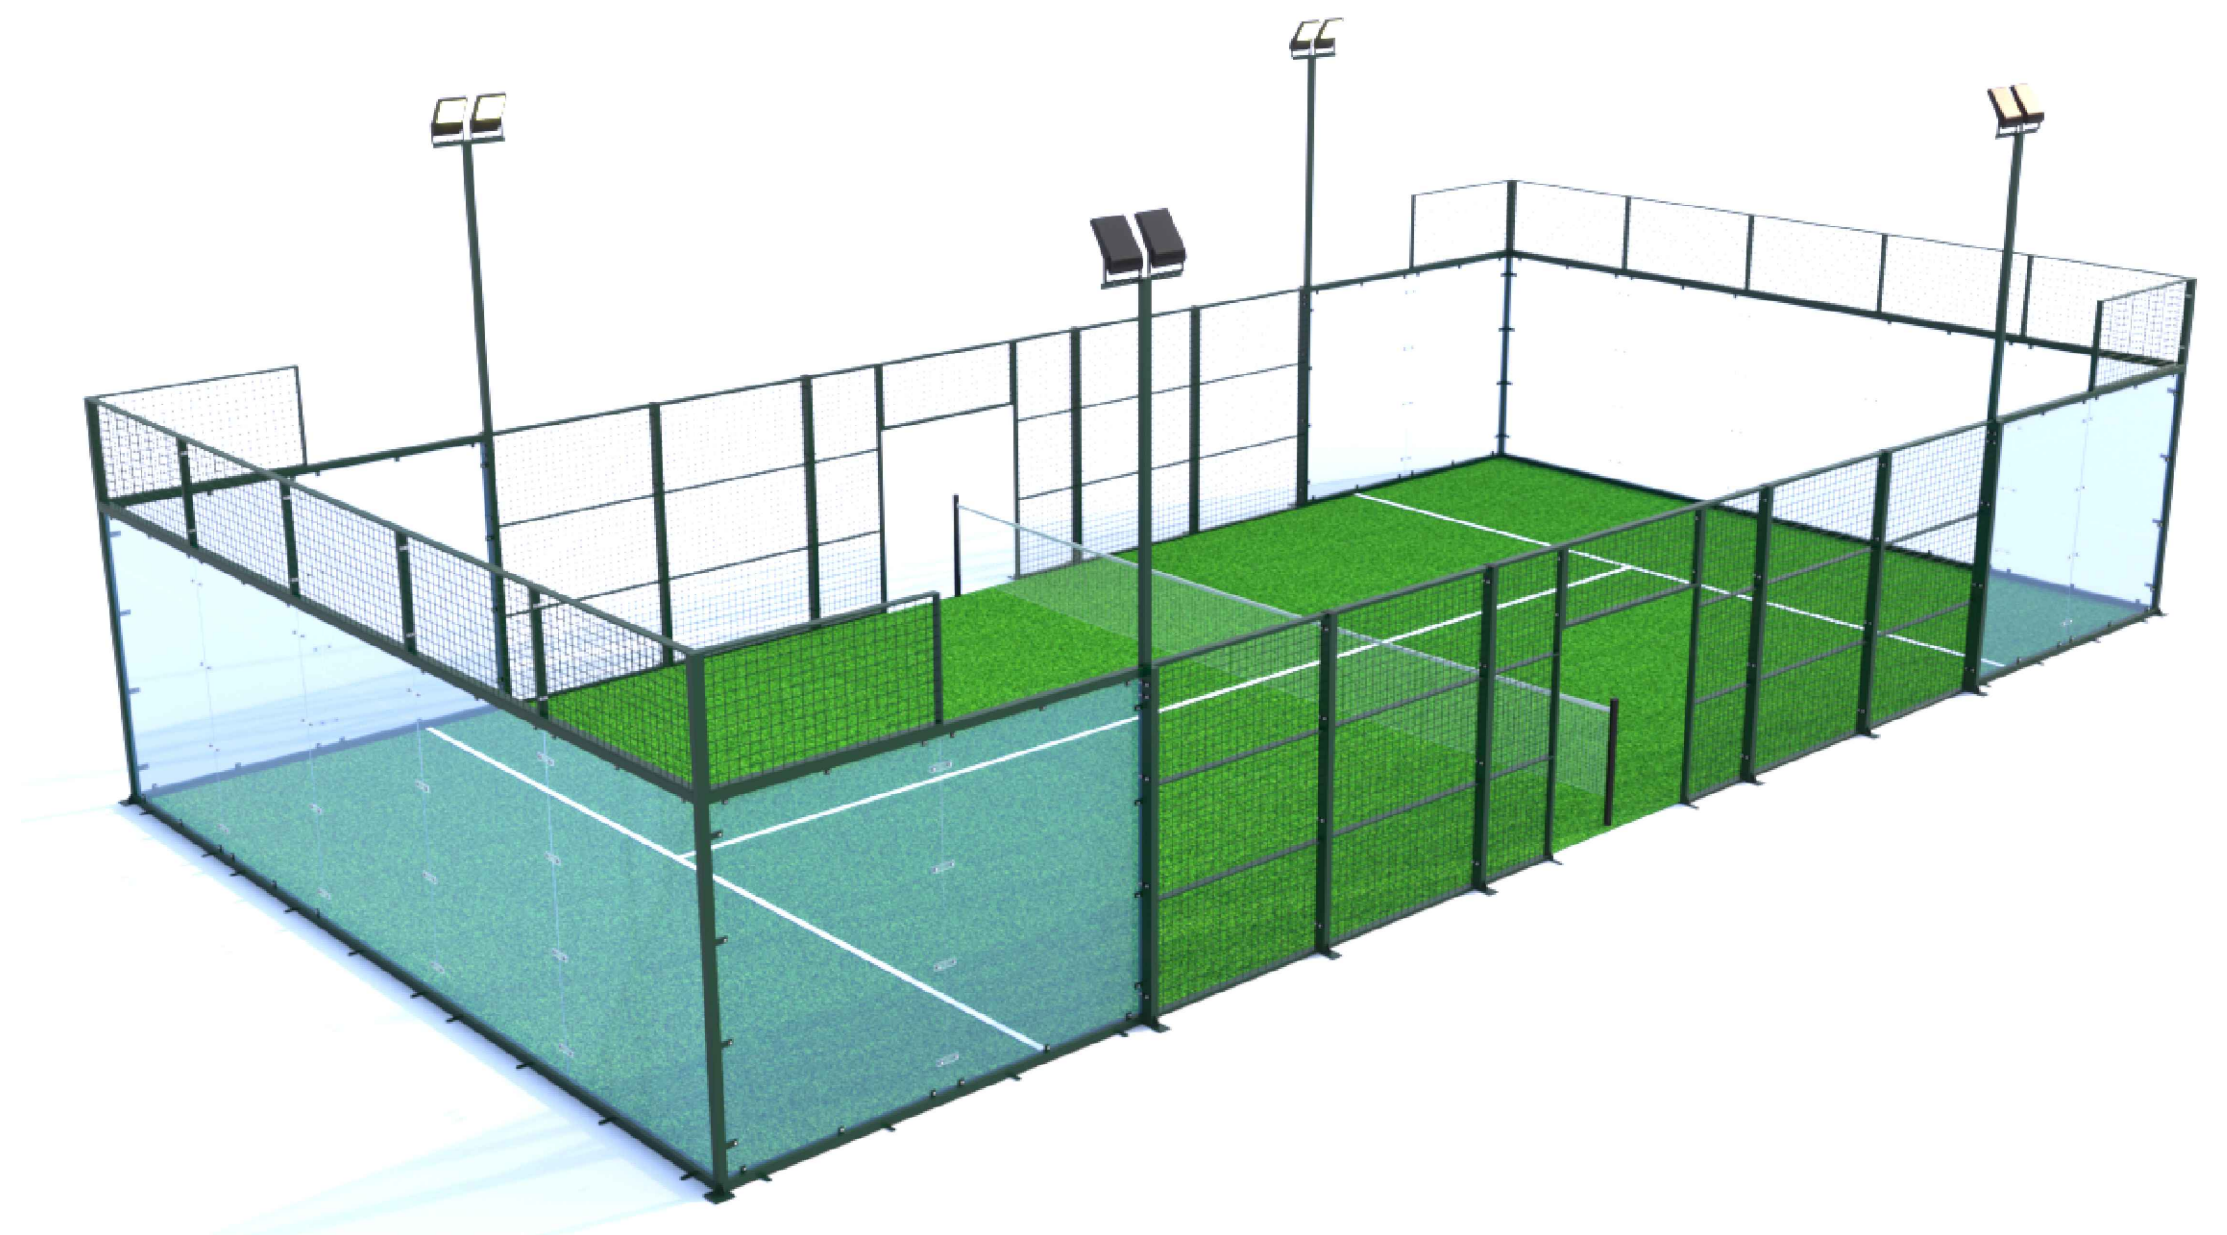


04 FE-19 - TYPICAL PADEL TENNIS DETAIL-REFERENCE IMAGE
09374 SPORTS HUB
Scale 1:50

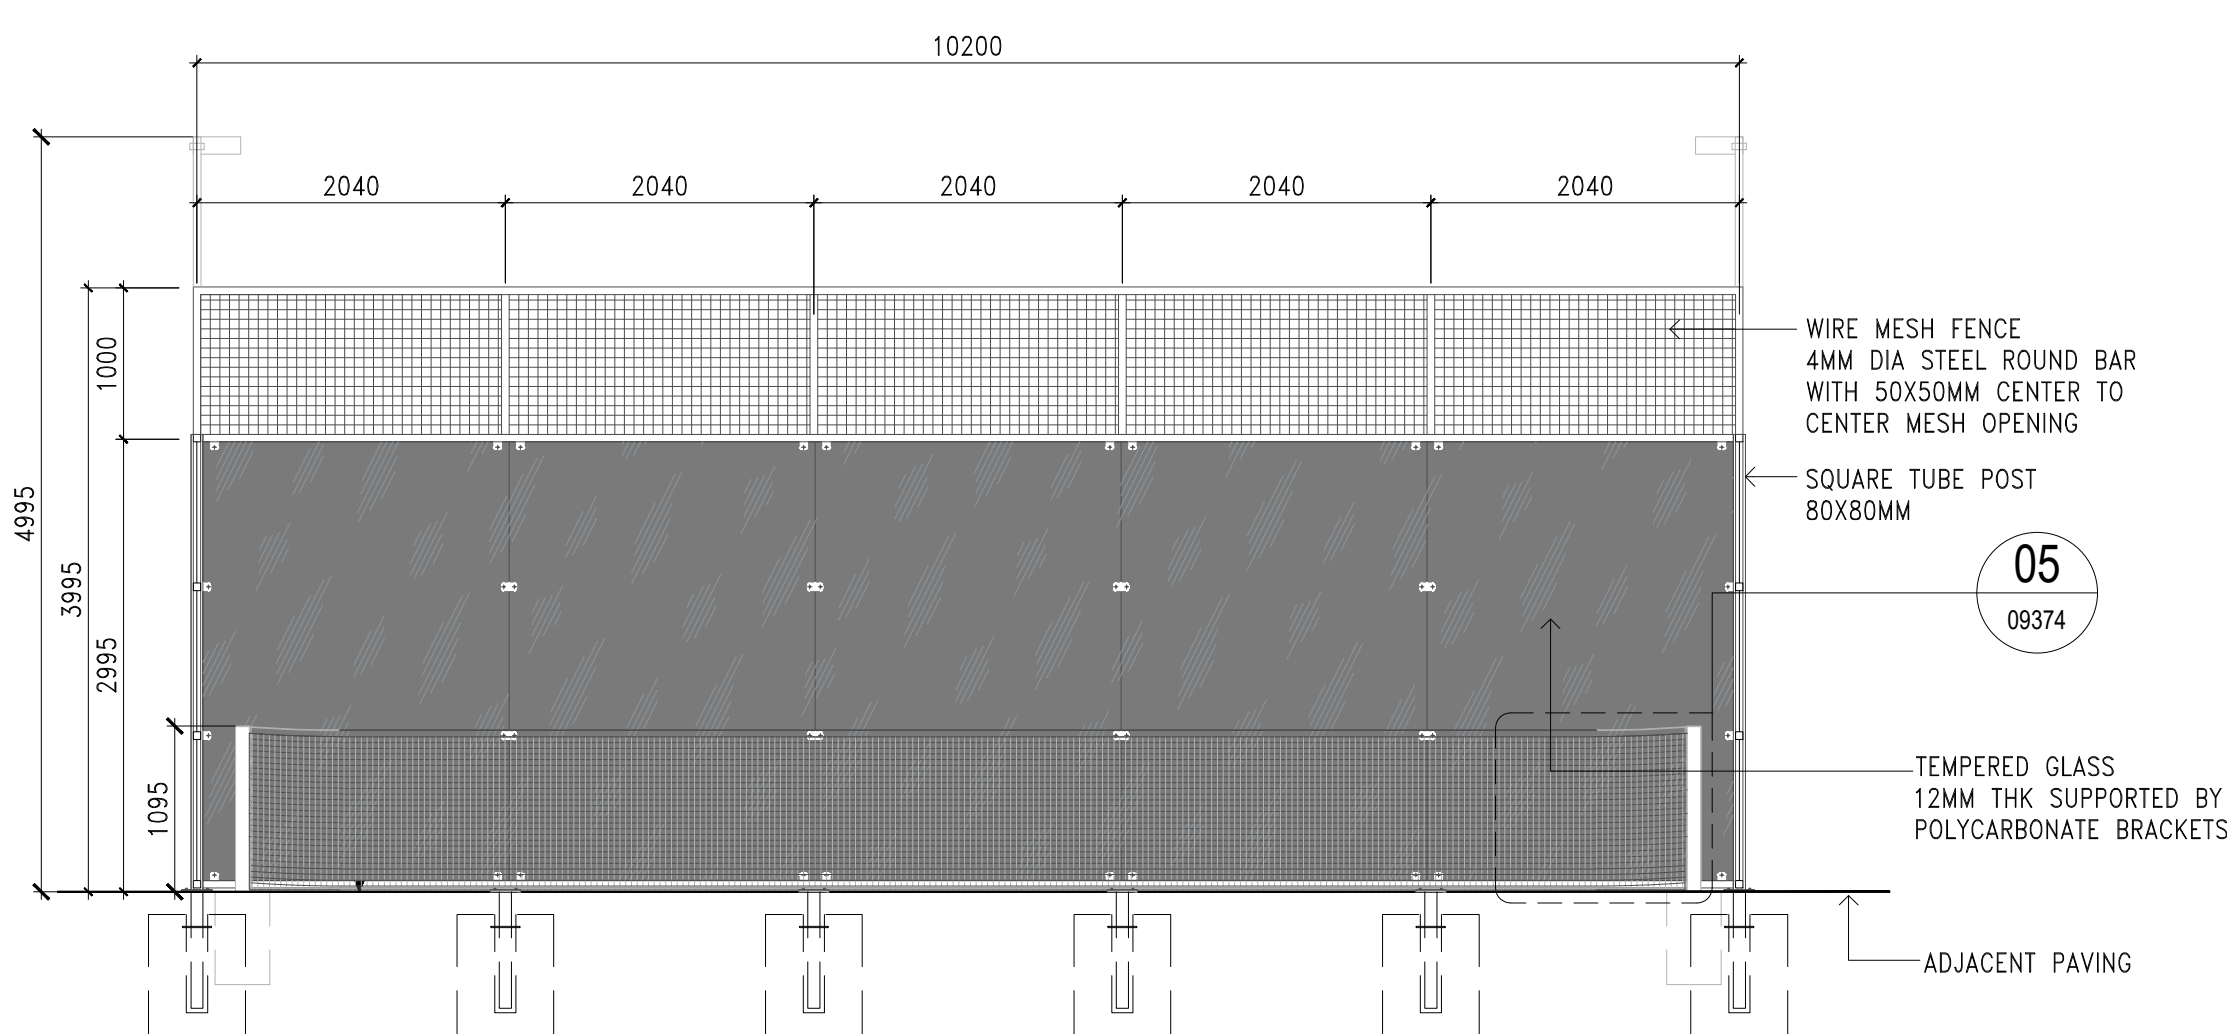

03 F07 - PADEL TENNIS FENCE DETAIL
09374 SPORTS HUB
Scale 1:50

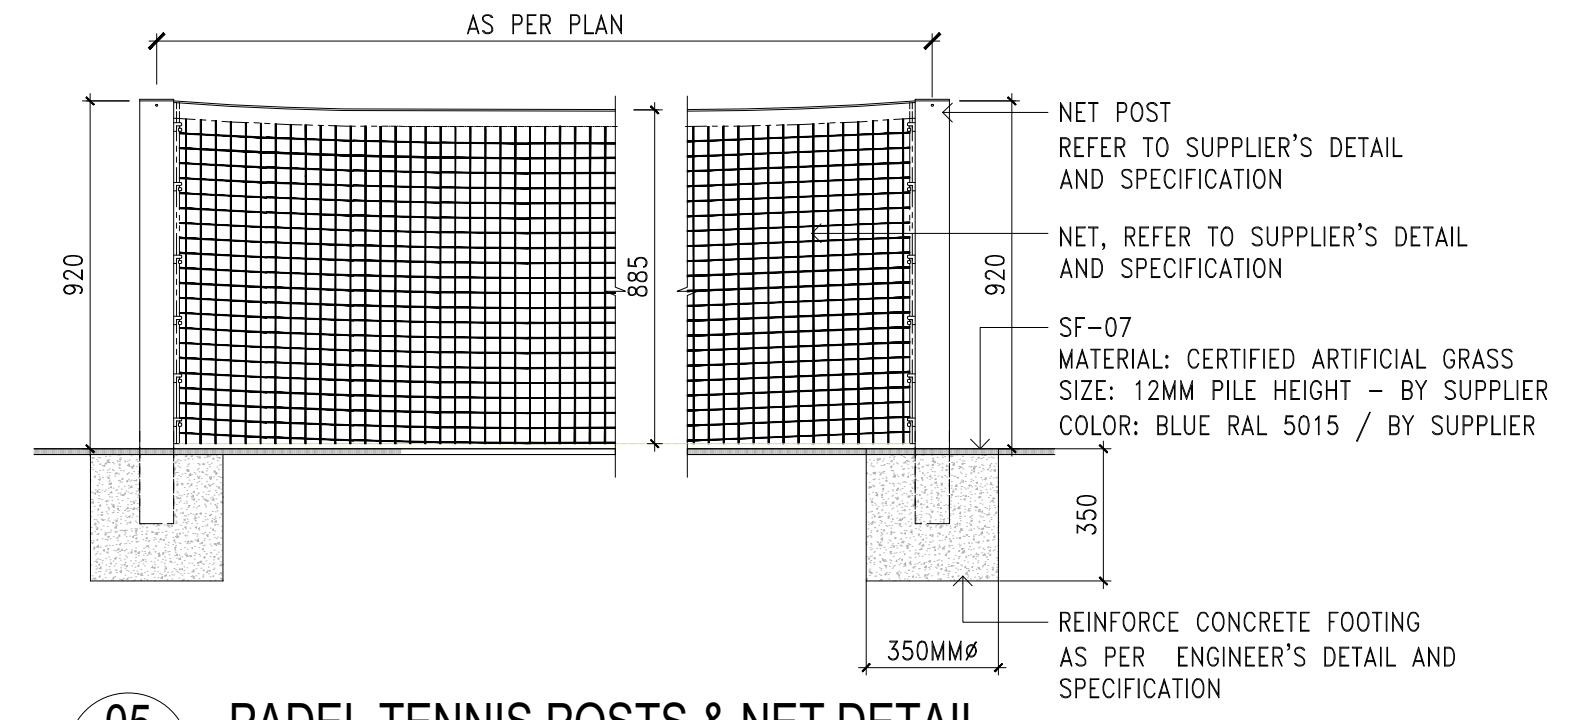

05 PADEL TENNIS POSTS & NET DETAIL
09374
Scale 1:20

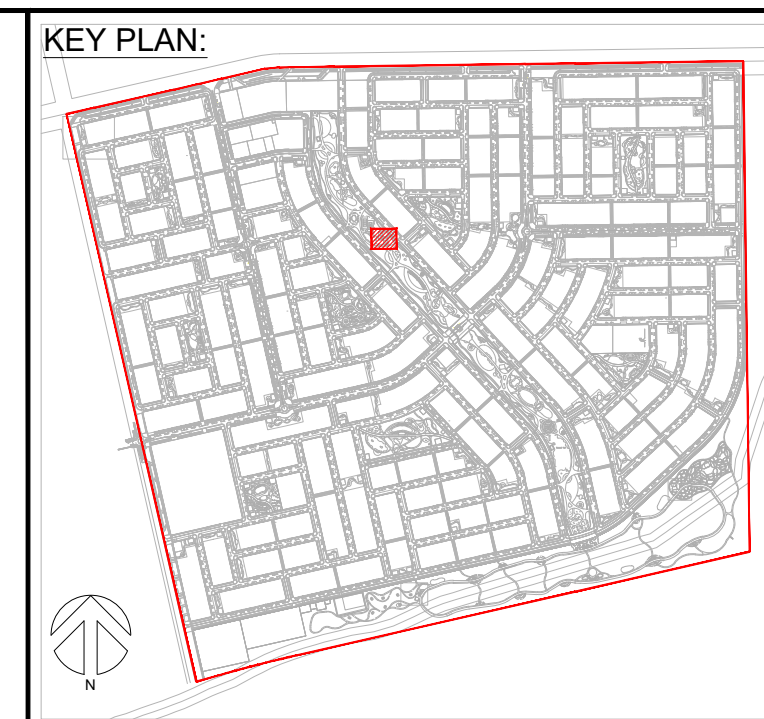

-	-	-
-	-	-
-	-	-
D00	PRELIMINARY DESIGN	XXX
REV	DESCRIPTION	DATE

DETAIL DESIGN

project
MEZYAD PARKS AND OPEN SPACES DEVELOPMENT

Client
ALDAR
Aldar Square, Yas Mall
P.O.Box 51133, Abu Dhabi, UAE
T: +971 80025327
web: <https://www.aldar.com/en>

Consultant
KEO
Sky Tower, 2nd floor,
Al Reem Island
P.O.Box 27594
Abu Dhabi City, U.A.E
T: +971 2 417 3000 F: +971 2 417 3001
web: <http://www.keo.com>
email: keo@keo.com

Dwg. Title
TENNIS COURT FENCE DETAIL

Scale:	1:4000@A1	Proj. Start Date:	APRIL 2025		
Drawn	CC	Arch/Engr	MW	Hd. A/E	RP
Proj. Dir.	CF	QA/QC	MA	PM	YG
Proj. No:	25-7023			Rev:	D00
Dwg. No:					