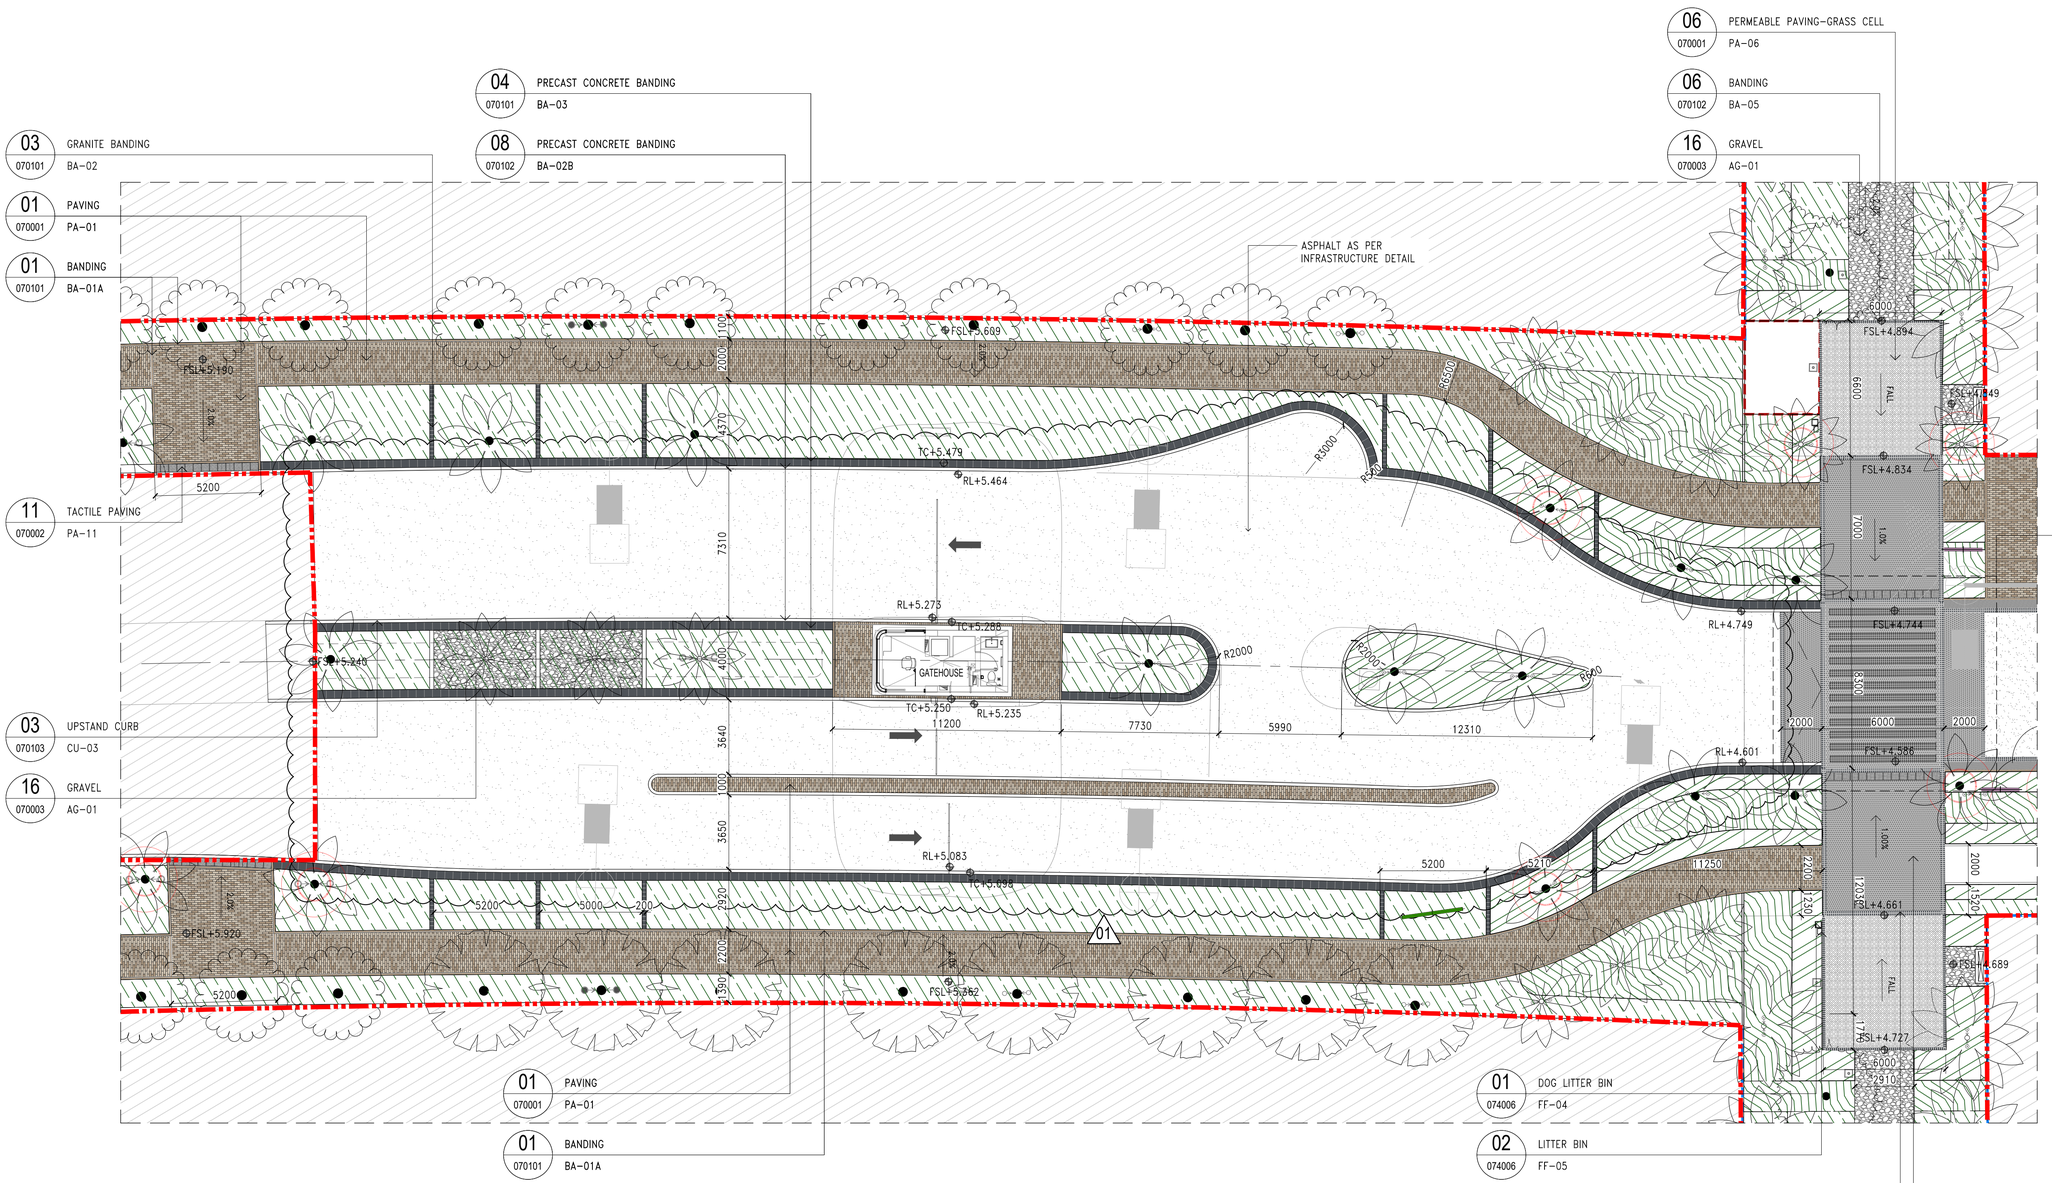

01 ENLARGEMENT PLAN - ARRIVAL EXPERIENCE

01 B50008 SCALE 1:150

LEGEND

PROJECT BOUNDARY; VILLA PLOT LINES; UTILITY PLOT LINES; STRUCTURAL PLOT LINES

SOFTSCAPE

TREES & PALMS; SUCCULENTS; PLANTING; LAWN; TREE WITH ROOT BARRIER

FURNITURES

FF-01 CABANA; FF-02 PERGOLA; FF-03 SWING; FF-04 DOG LITTER BIN; FF-05 LITTER BIN; FF-06 BIKE RACKS; FF-07 BOLLARD; FF-08 BENCH; FF-09 PICNIC TABLE AND SEATS; FF-10 HAMMOCK; FF-11 CABANA OUTDOOR SOFA

PLAY EQUIPMENT

PE-01 LIFE BY THE STREAM PLAYGROUND; PE-02 FLAMINGOGO PLAYGROUND; PE-03 ADVENTURES IN PARADISE

FITNESS EQUIPMENT

FE-01 JUNGLE WALK; FE-02 SPIRER PARALLEL BAR; FE-03 SPIRER MONKEY BAR; FE-04 SPIRER TRX-SHORT; FE-05 SPIRER BOX; FE-06 SPIRER MINI PARALLEL; FE-07 FITNESS PODS

HARDSCAPE

PA-01; PA-02; PA-03; PA-04; PA-05; PA-06; PA-07; PA-08; PA-09; PA-10/04; PA-11; RS-01; RS-02; WT-01; AG-01; SAND; ASPHALT; BA-01A/BA-01B; BA-02; BA-02B; BA-03; BA-04; BA-05; ME-01; S-01; CU-01; CU-02; CU-03; BL-01; W-01

SIGNAGE & WAYFINDING (BY OTHERS)

SIKKA ID; SIKKA OPERATIONAL SIGNAGE; VILLA ID - TYPE 1; VILLA ID - TYPE 2; FROND ID GATEHOUSE

LIGHTING (BY OTHERS)

LL1: 7M STREET POLE LIGHTS, 50W, 3000K.
LL2: WIDE BEAM UPLIGHTS FOR TREE, 12W, 3000K.
LL3: NARROW BEAM UPLIGHTS FOR PALM, 12W, 3000K.
LL4: RECESSED UPLIGHTS FOR CABANAS, 6W, 3000K.
LL5: LIGHT BOLLARD, 11W, 3000K.
LL7: POLE W/ INTEGRATED SPOTLIGHTS, 11W, 3000K.

F-01 FENCE 01; F-02 FENCE 02; FIRE HYDRANT; STREET LIGHT; ROAD SIGNAGE & MARKINGS; UTILITY MANHOLES

NOTE:

- R.O.W, CARRIAGEWAY, PARKING AND CURB DIMENSIONS ARE AS PER INFRASTRUCTURE INFORMATION.
- UNDERGROUND AND SURFACE UTILITIES ARE AS PER INFRASTRUCTURE INFORMATION.
- CURBS AND OTHER ROAD DETAILS AND SPECIFICATIONS ARE AS PER ROAD ENGINEERS.
- LIGHTING AND SIGNAGE &WAYFINDING LAYOUT ARE AS PER CONSULTANTS INFORMATION.
- CONTRACTOR TO VERIFY ALL EXISTING SITE CONDITIONS PRIOR TO COMMENCING ANY LANDSCAPE WORKS.
- FOR LANDSCAPE GENERAL NOTES, REFER TO PJA-SIE-STW-FRS-ZZZ-DWG-LSC-00002

ORIGINAL PAPER SIZE: A1 (841x594mm)

CLIENT

DUBAI HOLDING

PROJECT MANAGER

TiME

CONSULTANT

STUDIOI

CONSULTANT

IN SITE

P.O.Box 49100, Dubai, UAE. 31st Floor Rolex Tower Sheik Zayed Road.
Tel.: (971) 43888440. Fax: (971) 43888440
web: http://www.insitc.com email: ias@insitc.com

"ISSUED FOR"	"DESCRIPTION"
FA FOR APPROVAL	100% ISSUED FOR CONSTRUCTION

NO	DATE	DESCRIPTION	REV BY
01	22-MAY-2026	ISSUE FOR CONSTRUCTION	WK
00	27 MAR 2026	100% ISSUED FOR CONSTRUCTION	WK

STAMPS

KEYPLAN

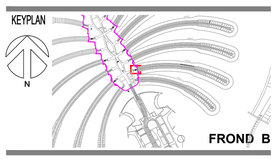

PALM JEBEL ALI

FROND - B

PALM JEBEL ALI, DUBAI, UAE

Landscape Design

ARCHITECT	BORAN AGOSTON	REG NO.	106893
STRUCTURAL ENGINEER	OMAR SHAFIQ	REG NO.	85059

PROJECT NO.	P192
PROJECT MANAGER	WK
PROJECT ARCHITECT	RC
DRAWN BY	RS
CHECKED BY	RC
SCALE AT ISO A1	1:150

PJA-SIE-STW-FRB-ZZZ-DWG-LSC-B50008

FROND B ENLARGEMENT PLAN - ARRIVAL EXPERIENCE

SHEET ISSUE DATE 23/5/2026 4:33:58 am