


This document and the information contained herein are the property of QIC. No part of this document may be reproduced, stored, transmitted, or distributed in any form or by any means, electronic, digital, or otherwise, without the prior written consent of QIC. Except as expressly agreed by QIC in writing, QIC shall not be responsible or liable for any loss (direct, consequential, or otherwise) arising from reliance on or use of this document or the information contained herein.

Key Plan:

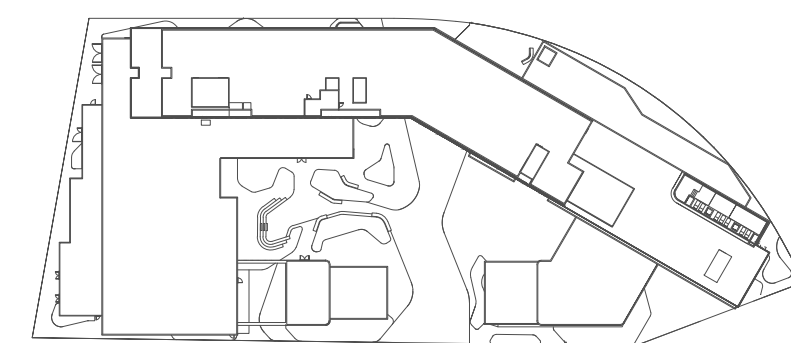

Notes:

1. THIS DRAWING IS THE COPYRIGHT OF JT+PARTNERS AND MUST NOT BE RETAINED, COPIED OR USED WITHOUT THE ABOVE CONSULTANT'S AUTHORITY.
2. DO NOT SCALE FROM THE DRAWINGS.
3. ALL DIMENSIONS ARE IN MILLIMETERS AND LEVELS IN METERS UNLESS NOTED OTHERWISE. ALL DIMENSIONS TO BE VERIFIED ON SITE & APPROVED BY THE ENGINEER.
4. THIS DRAWING SHOULD BE READ IN CONJUNCTION WITH OTHER RELEVANT ARCHITECTURAL, STRUCTURAL, MECHANICAL, ELECTRICAL, LANDSCAPE AND INTERIOR DESIGN DRAWINGS AND ALL RELEVANT SECTIONS OF THE SPECIFICATIONS.
5. CONTRACTOR TO ENSURE THAT ALL MATERIALS TO COMPLY WITH THE LATEST SBC CIVIL DEFENCE REQUIREMENTS.
6. THIS DRAWING DOES NOT RELIEVE THE CONTRACTOR OF PROVIDING SHOP DRAWINGS FOR APPROVAL BEFORE COMMENCING ANY WORK ON SITE.

LIST OF REFERENCE DRAWINGS

Sr. No.	Drawing Number	Rev. No.

ENGINEER'S REVIEW STATUS & STAMP

- A - Approved
B - Approved with comments
C - Revised and Resubmit
D - Rejected


OC	50% SCHEMATIC DESIGN SUBMISSION	08/06/2026	JTP
Rev. No.	Revision Description	Rev. Date	Approved by

Revision Schedule

Client:



Lead Design Consultant:

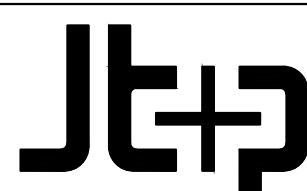

JT & PARTNERS ARCHITECTURAL AND ENGINEERING CONSULTANT
DUBAI P.O.Box 413606, Tel: +971 (0)4 452 1135 www.jtpartners.com

Sub Consultant:

Architect of Record:



Project Location:
D12-RESORT CORE DISTRICT-WEST VILLAGE SOUTH PACKAGE 1B
QIDDIYA ENTERTAINMENT CITY/ QIDDIYA COAST

Project Title:
QIDDIYA WEST VILLAGE SOUTH


Purpose of Issue:

50% SCHEMATIC DESIGN SUBMISSION

Drawing Title:

THEME PARK WATER FEATURE


Authored By: INSITE	Checked By: Checker	Scale: 1 : 25 @A0	Issue Date: 08/06/2026
Model File Reference: QC00912034-JTP-C05037-MOD-LSE-00-000XX1-0000100			Revision No.: OC
Drawing No.: QCR001-JTP- C05037- DRW- LSE- 00- 000XX1- 3GF1002			

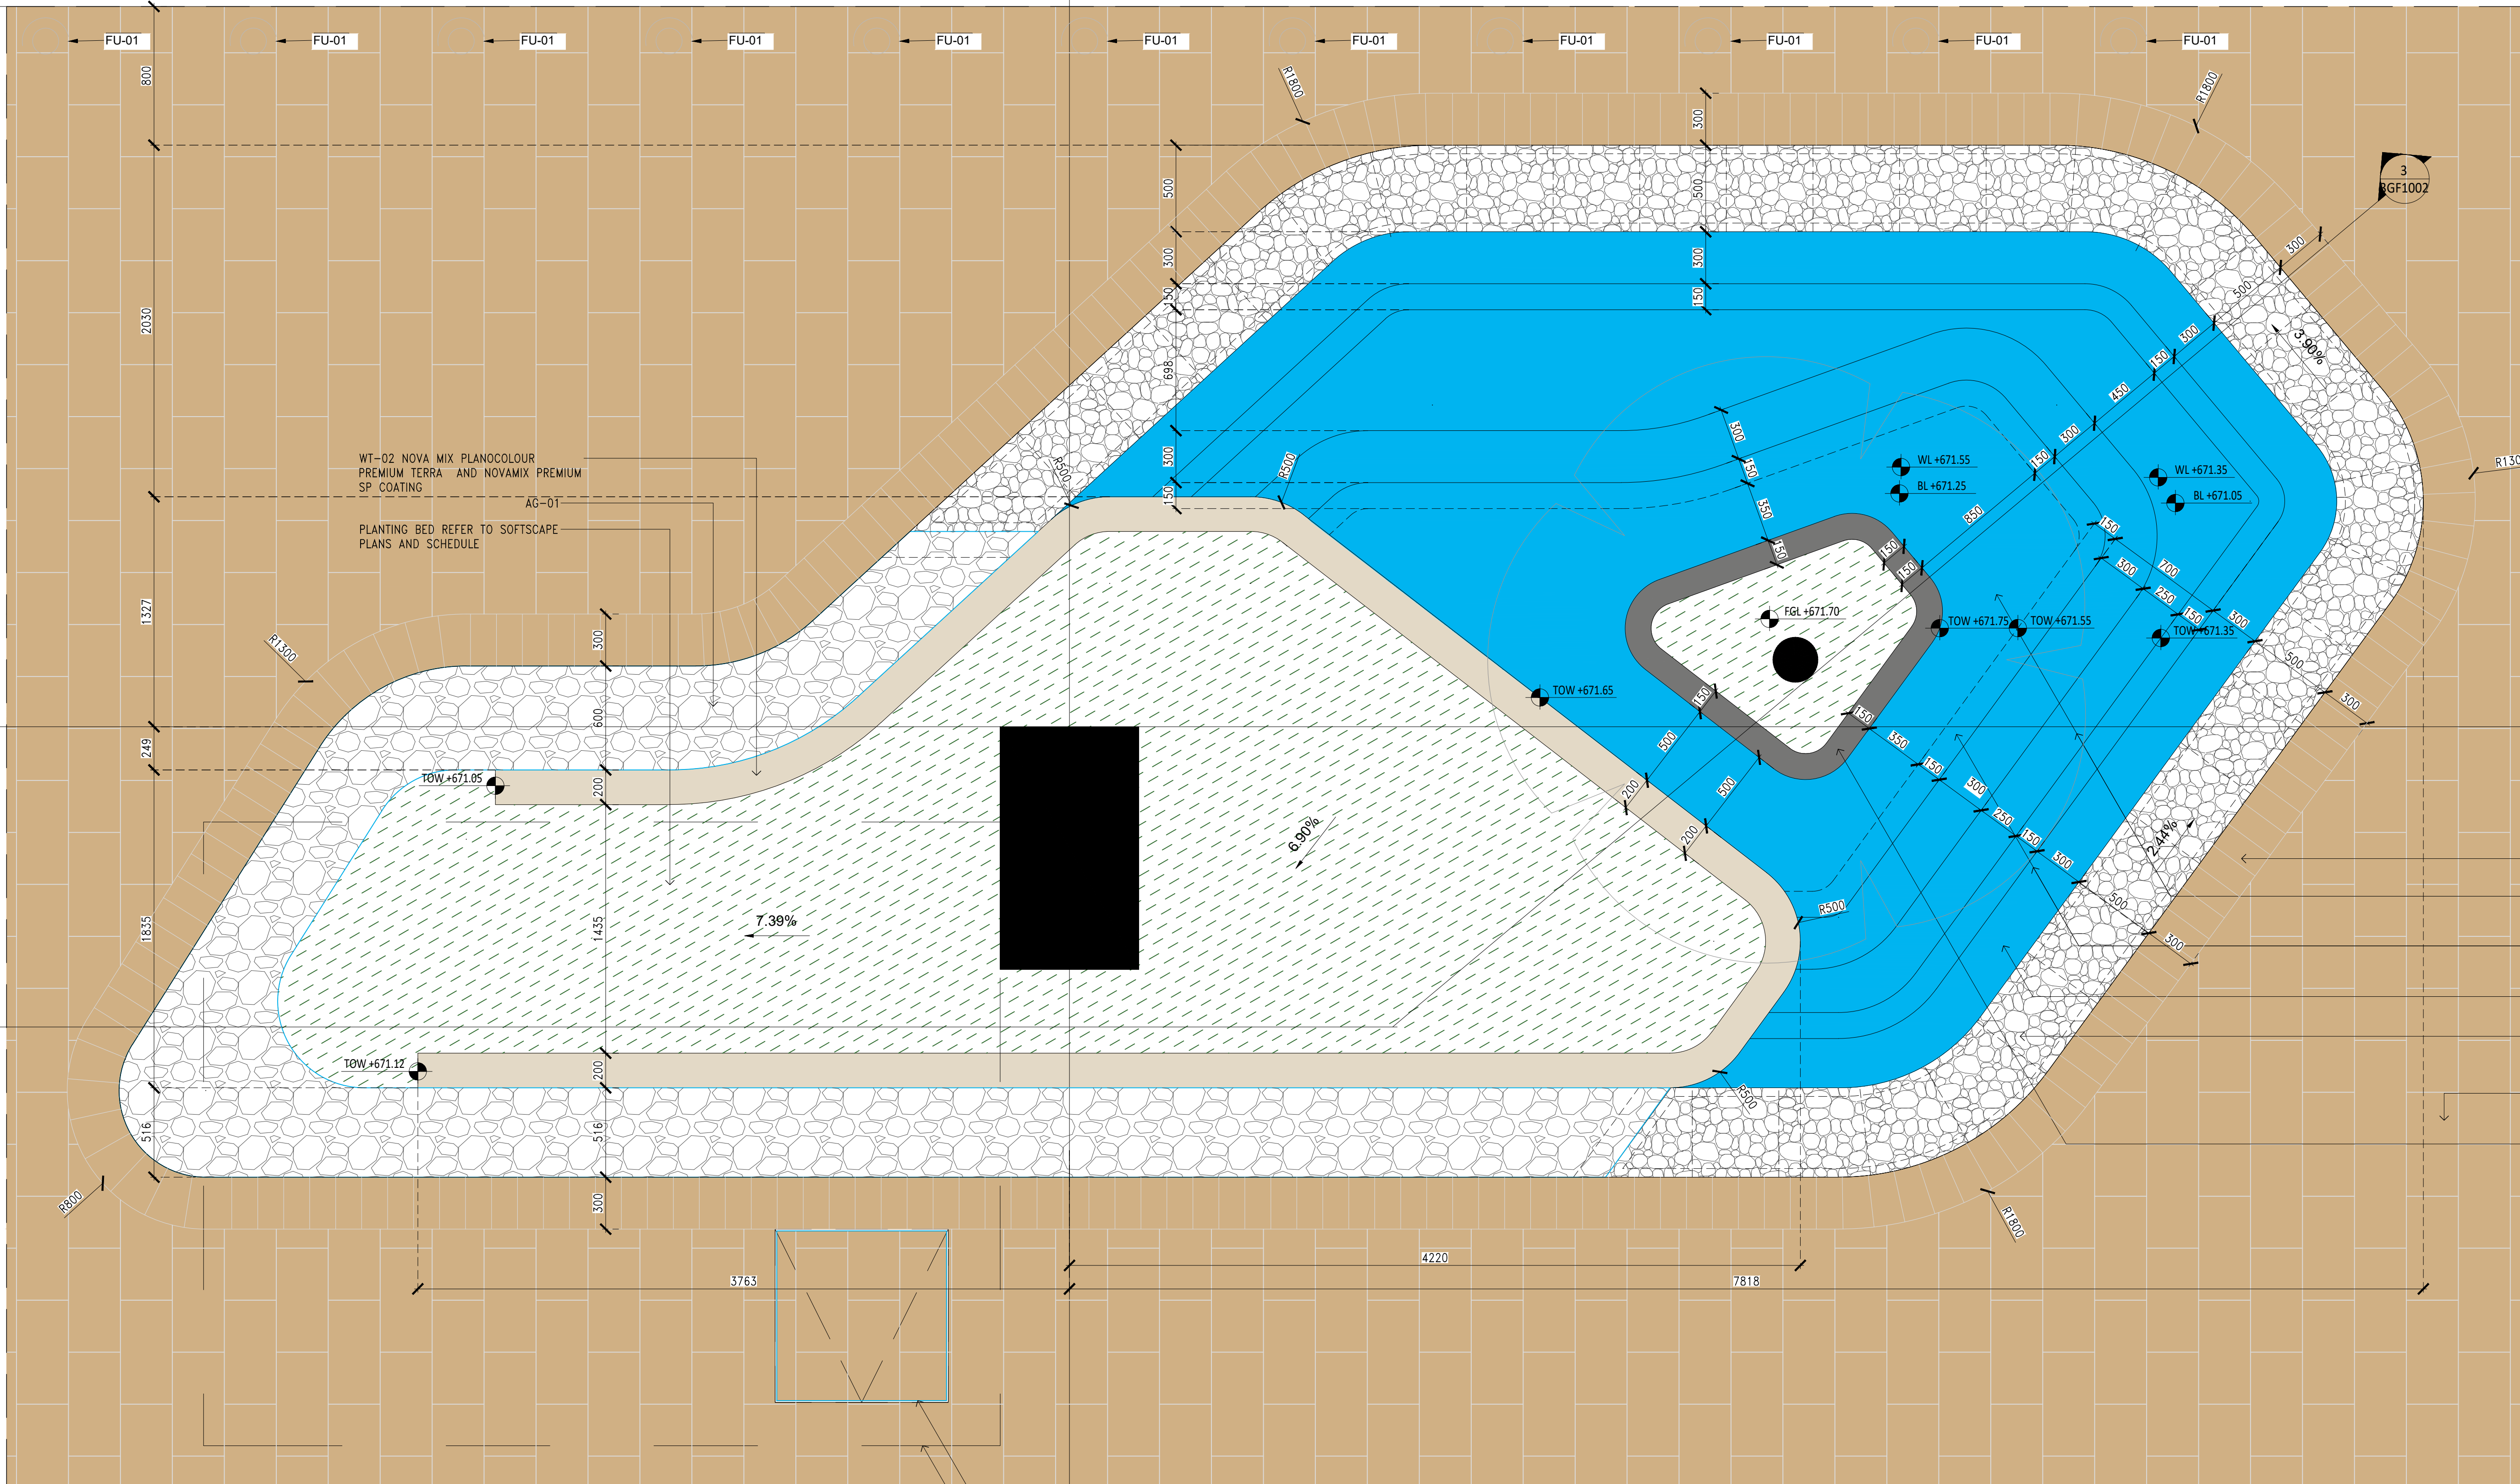

- ET-02 CONCRETE FLUSH EDGING
WS-02 NOVA MIX PLANOCOLOUR PREMIUM TERRA AND NOVAMIX PREMIUM SP COATING
WT-02 NOVA MIX PLANOCOLOUR PREMIUM TERRA AND NOVAMIX PREMIUM SP COATING
CT-03 20MM THK GRANITE CUT TO SIZE, ABSOLUTE BLACK
AG-01
PV-01 PEDESTRIAN PAVING 01
CT-03 COPING TYPE 03 GRANITE ABSOLUTE BLACK

01 WATER FEATURE-01


SCALE: 1:20

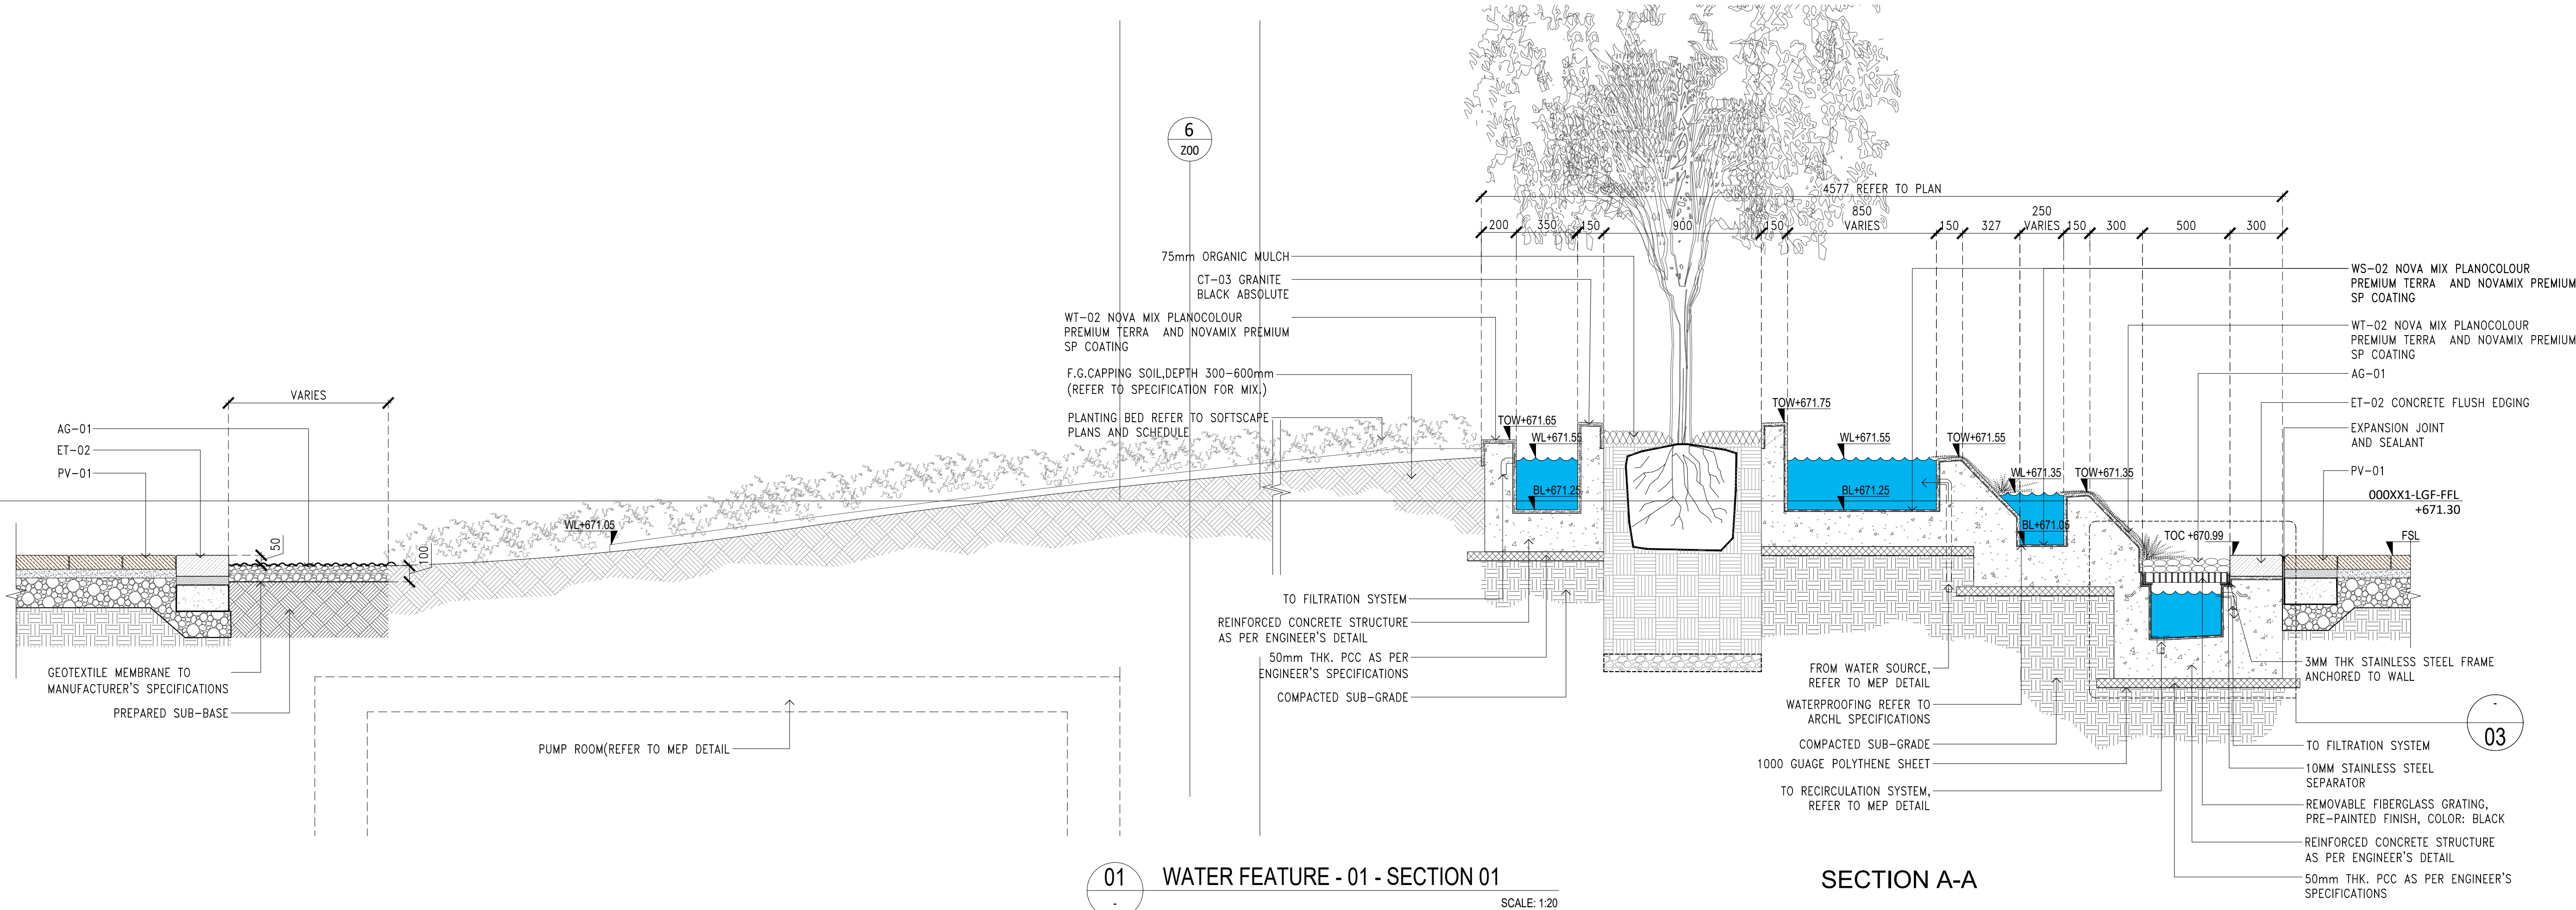

01 WATER FEATURE - 01 - SECTION 01

SCALE: 1:20

SECTION A-A

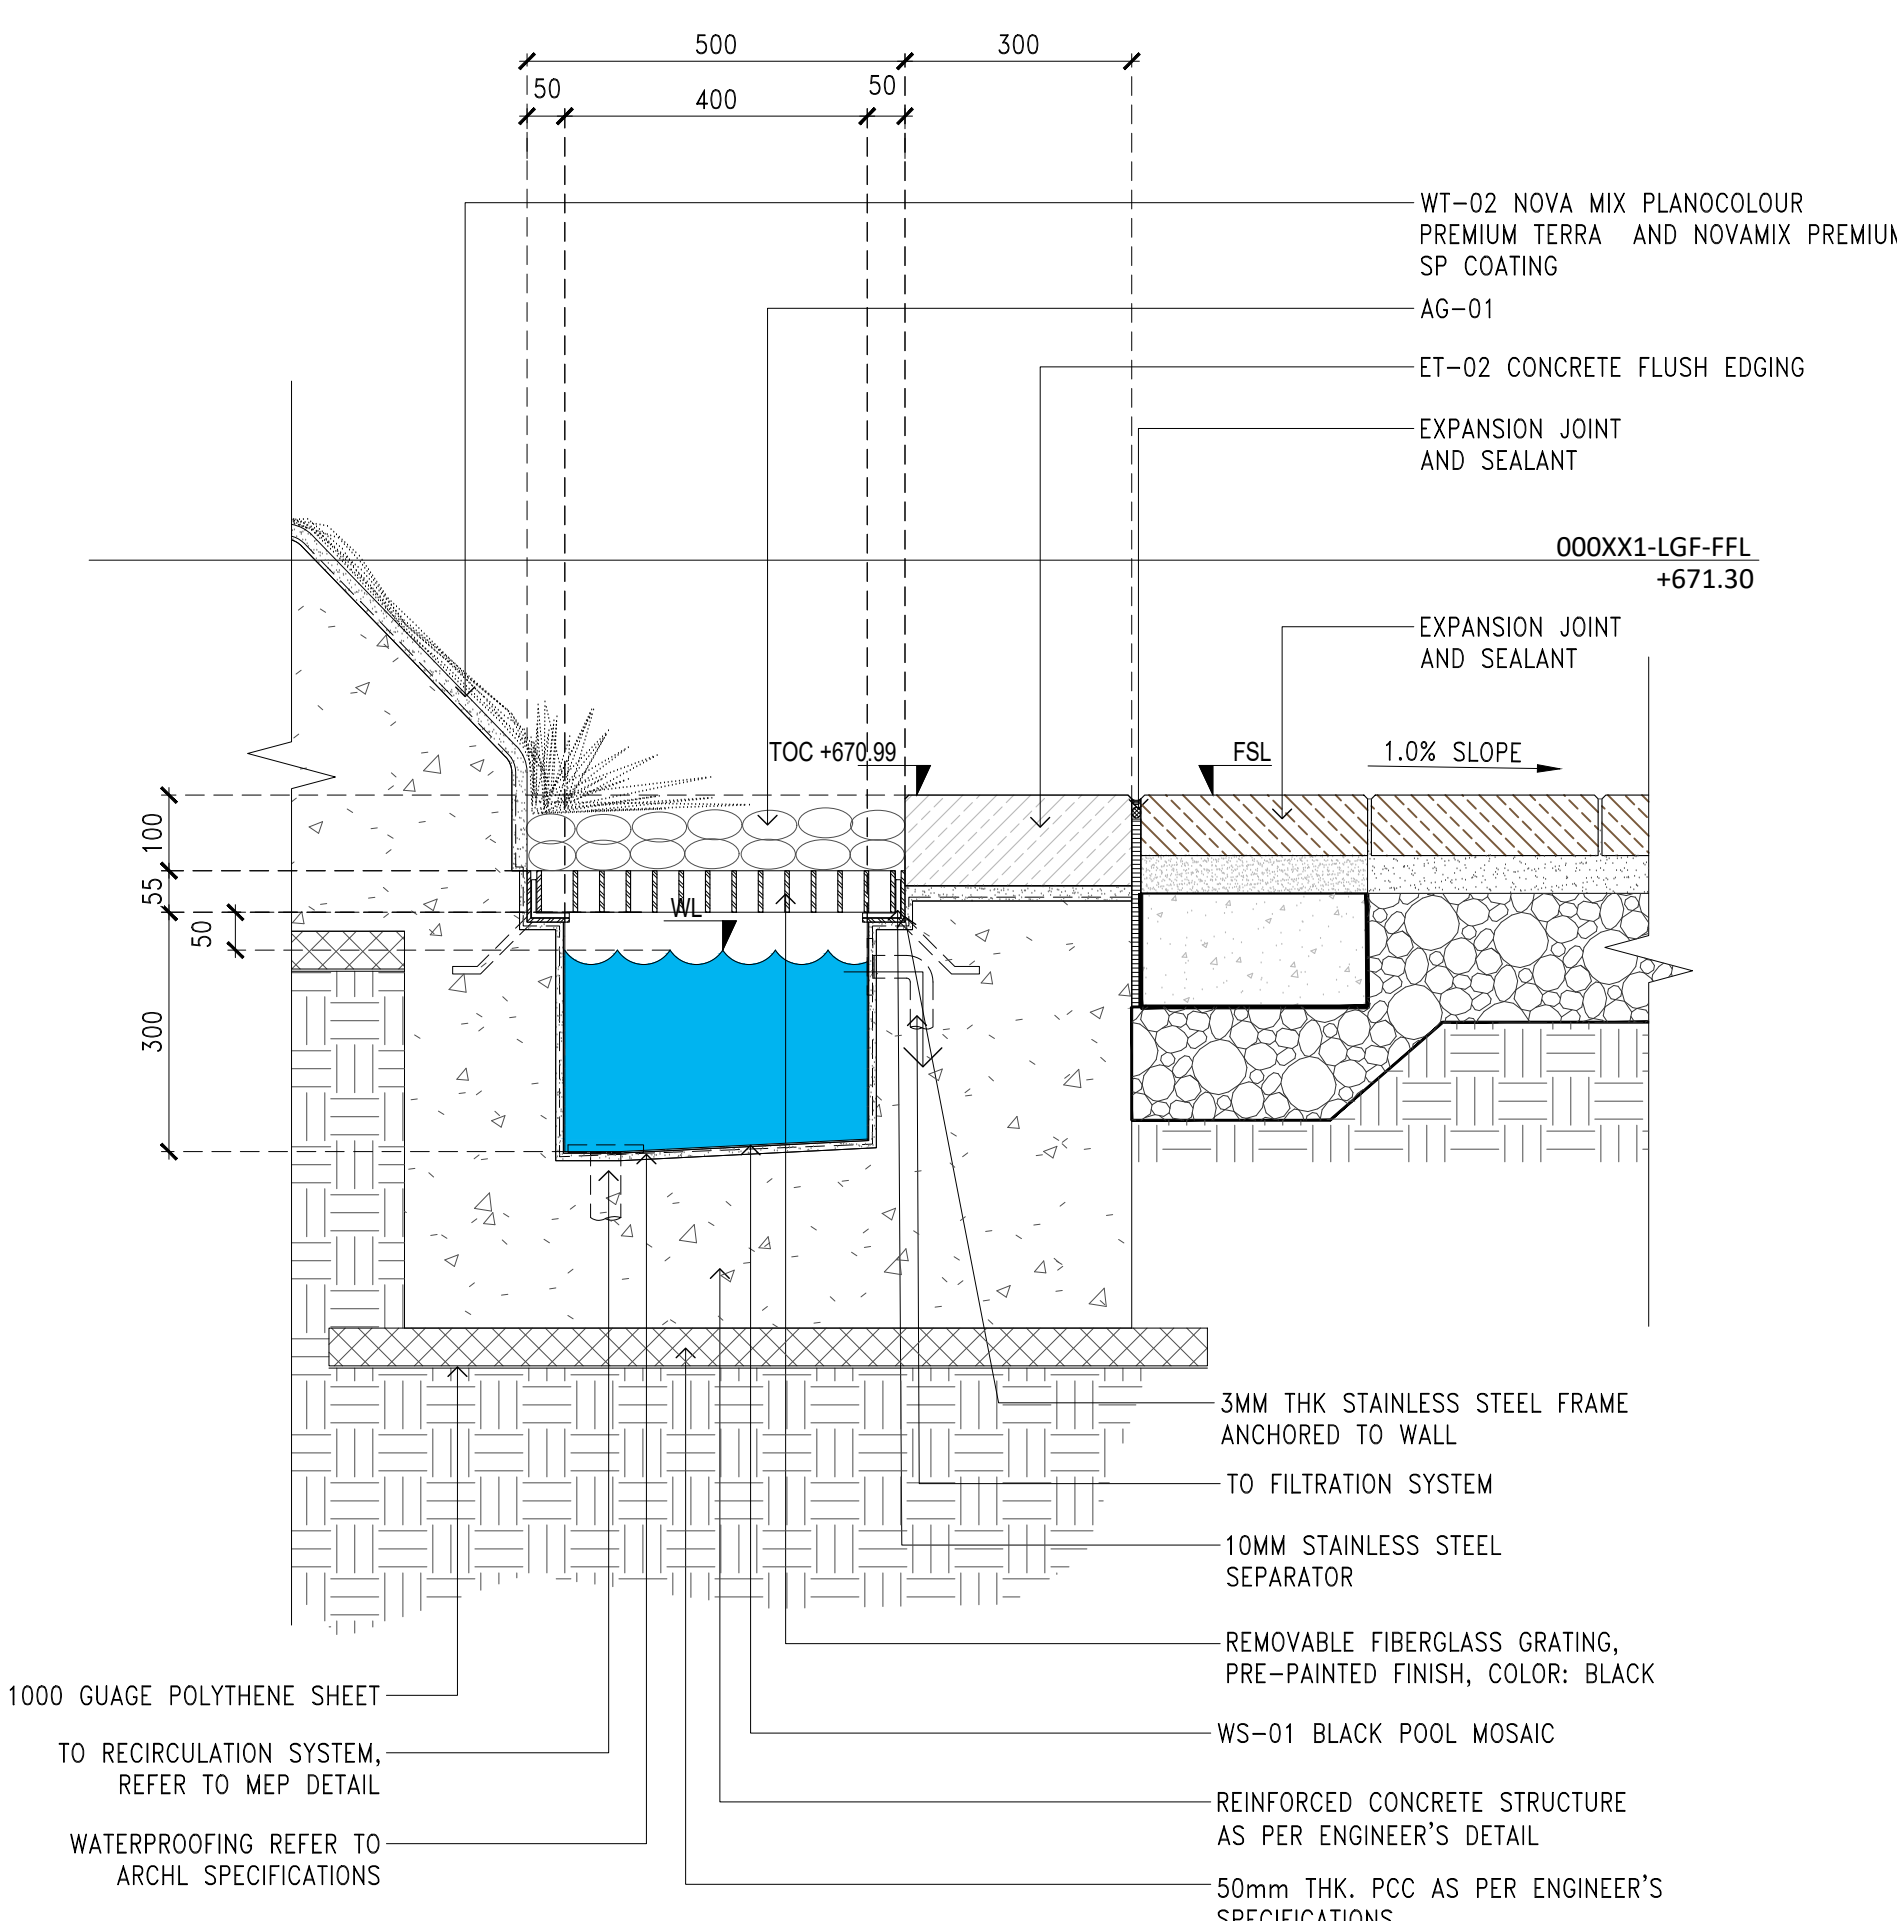

33 WATER FEATURE - 01 - SPOT DETAIL